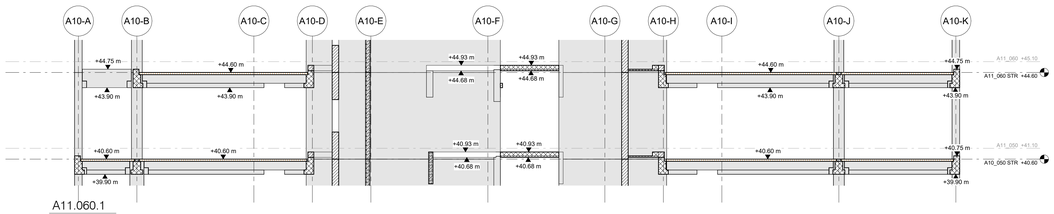

A11.060.1
1 : 100

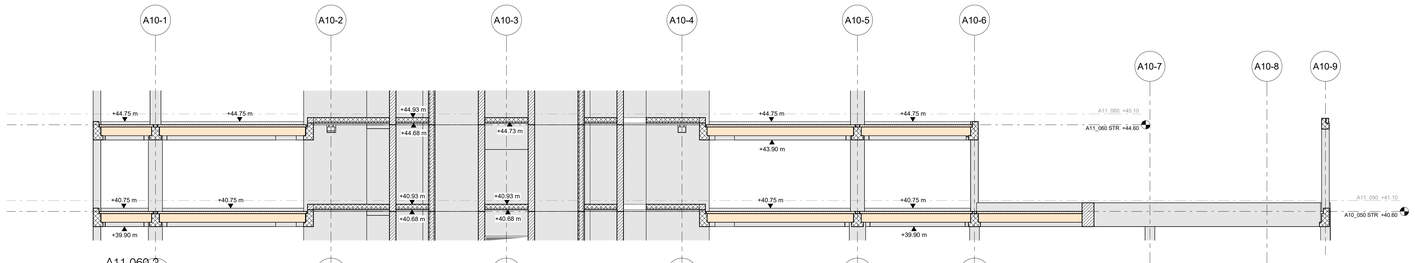

A11.060.2
1 : 100

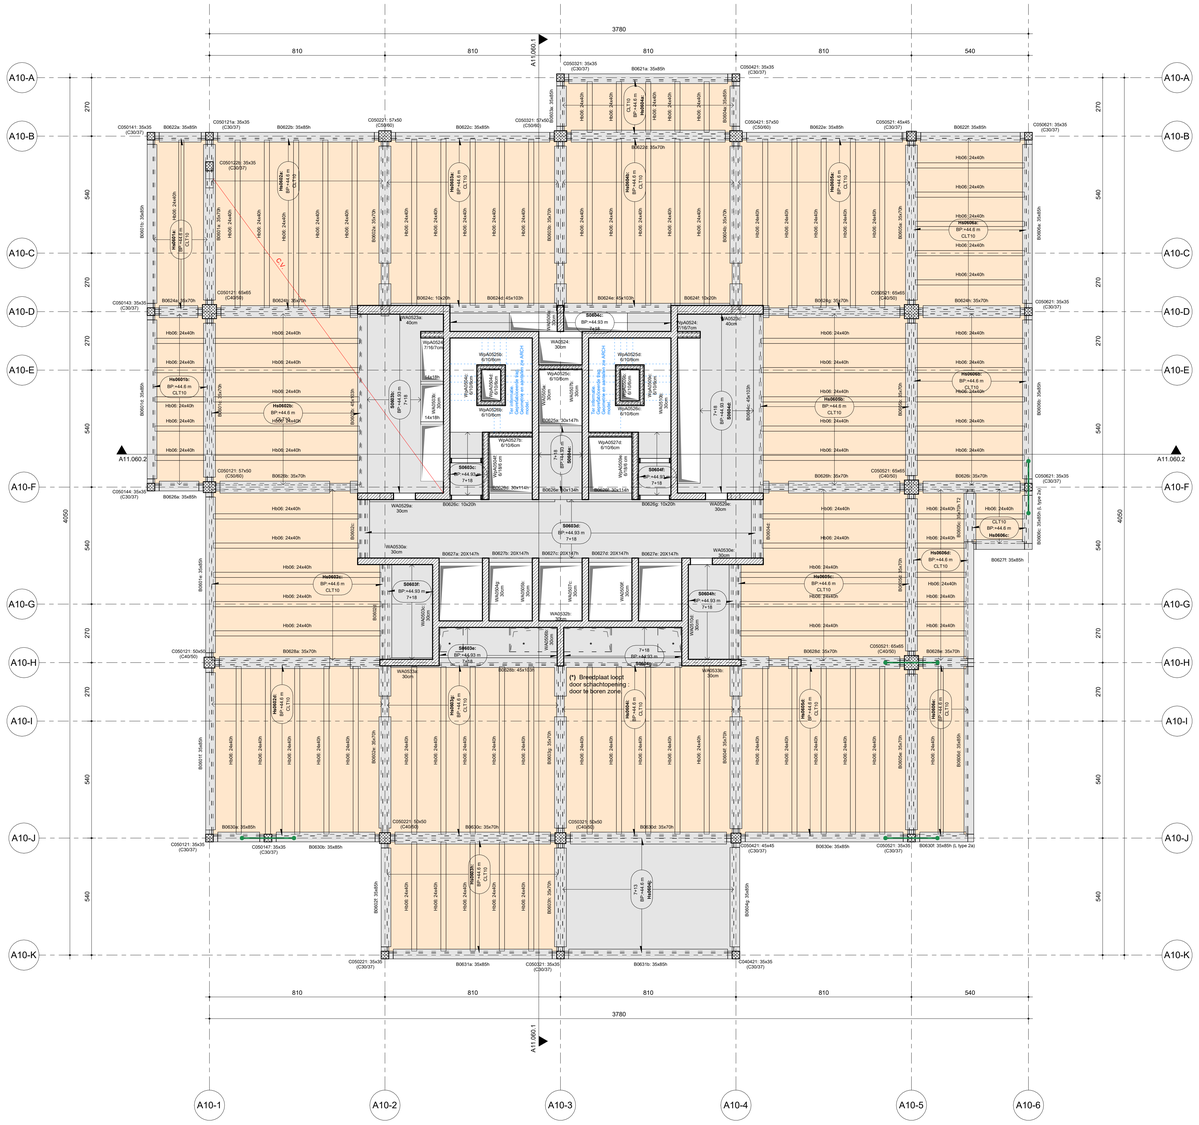

P060 - Afdek050
1 : 100

TEKENCONVENTIE

Norm ISO 128-40:2013 - Type B

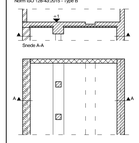

NAAMGEVING VAN STRUCTURELE ELEMENTEN

P:	PAAL	W:	WAND
Pk:	PAALKOP	C:	KOLOM
Fo:	FUNDERINGSBALK	B:	BALK
Z:	ZOOL	S:	VLOERPLAAT
Vp:	VALSE PUT	L:	LINTEEL / LATEI
		M:	METSELWERKMUUR (dragend)

VLOERPLAAT SCHACHT

LEGENDE MATERIALEN

- TER PLAATSE GESTORT BETON (gesneden)
- TER PLAATSE GESTORT BETON (aanzicht) — Bovenaanzicht: dikte volgens aangrenzende verdieping.
- GEPREFABRICEERD BETON (gesneden)
- GEPREFABRICEERD BETON (aanzicht) — Bovenaanzicht: dikte volgens aangrenzende verdieping.
- BOVENLIGGENDE BETONSTRUCTUUR
- HOUTEN STRUCTUUR
- METSELWERKMUUR UIT KALKZANDSTEEN (dragend)
- DRAGEND METSELWERK
- BOVENLIGGEND METSELWERKSTRUCTUUR (dragend)
- NIET-DRAGEND METSELWERK — Alleen te tekenen indien nodig om het plan te begrijpen.

20	24	20	15+5/7	6+14	(80+5/8)	(16+4)1	20
Grondplaat 30cm	Geprefabriceerd element 24cm	Ter plaatse gestorte plaat 20cm	Welfsels 15cm = min 5cm TPGB met 2cm tegenpeil	Breedvloerplaat 6cm + 14cm TPGB	TT elementplaat 80cm + min 6cm TPGB met 2cm tegenpeil	Houten constructievloer 16cm + 4cm TPGB	Staal-betonplaat 20cm

ELEMENTEN IN TER PLAATSE GESTORT BETON

	Omgevingsklasse	Sterkteklasse
Palen	EA1	C30/37
Bezaagpalen	EA1	C30/37
Paalkoppen	EE1	C30/37
Funderingszolen	EE1	C30/37
Funderingsplaat en grondvloerplaat	EE3	C25/30
Voegsteiten	EI	C30/37
Druklaag op welfsels (ondergrond)	EI / EE4	C30/37
Druklaag op breedplaten	EI	C30/37
Wanden (opsplitsing intervieelem)	EI / EE3	C30/37
Wanden (grondgekend en ondergronds)	EE2	C30/37
Wanden (keris)	EI	C30/37
Kolommen boven- en ondergronds	EI / EE2	C30/37
Balken boven- en ondergronds	EI / EE2	C30/37
Consoles	EI	C30/37

VOORBEELD : B AXYYz: a x bh

B ELEMENT
A PREFIX
X VERDIEPING
YY NUMMER
z SEGMENT

a dikte
b hoogte

PEILEN & OPENINGEN

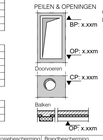

Openingen: BP en OP zie plancht
Doorvoeren: OP ze aanzichten

GEPREFABRICEERDE BETONNEN ELEMENTEN

	Omgevingsklasse	Sterkteklasse
Kolommen en ondergrondse kolommen	EI / EE4	C40/50
Balken en ondergrondse balken	EI / EE4	C40/50
Welfsels	EI / EE4	C50/67
Breedplaten	EI	C30/37
Trappen	EI	C30/37

MECHANISCHE BEVESTIGING

	Bouldiaasie
Klassieke bouten	8.8
Voorgespannen bouten	10.9

ELEMENTEN IN STAAL

	Staalkwaliteit	Corrosiewiltscategorie en duurzaamheidscategorie	Corrosiebescherming	Brandbescherming
In beton gestort profielen	S235 JR	C1 / H	/	/
Staalprofielen (binnen)	S235 JR	C1 / H	Afwerkingsverf	Opschuimende verf (R60) / gipsplaat (R60/120)
Staalprofielen (buiten)	S235 J2	C3 / H	Afwerkingsverf	Opschuimende verf (R60) / gipsplaat (R60/120)

NOTA

- De afmetingen dienen door de architect en de aannemer gecontroleerd en goedgekeurd te worden ;
- De openingen voor technische doorvoeren zijn steeds indicatief. Voor het opstellen van de wapeningsplannen moeten de definitieve de afmetingen en inplanting van deze openingen door de aannemers gegeven en goedgekeurd worden in coordinatie met de uitvoerders van de technieken ;
- De aannemer voorziet alle nodige openingen van technische installaties en hun ondersteuningen voorzien worden ;
- De aannemer voorziet waterkeringsplaten tussen elke 2 stortfasen ondergronds ;
- De aannemer bepaalt het bovenpeil van de opleggenstelles rekening houdende met tegenpeil van de welfsels of andere geprefabriceerde elementen ;
- De stabiliteitsplannen werden opgesteld op basis van de architectuur plannen en modellen beschikbaar op 21/10/2024.

BRANDVEILIGHEID

- Tenzij anders vermeld beantwoordt de brandweerstand van de structurele elementen aan het Koninklijk Besluit voor de preventie van brand :
  - ~~voor lage gebouwen: R60 voor alle structurele elementen behalve het dak; R60 voor de structurele element van het dak ;~~
  - voor middelhoge gebouwen: R120 voor alle structurele elementen onder het evacuatieniveau; ~~R60 voor alle structurele elementen boven het evacuatieniveau ;~~
  - voor hoge gebouwen: R120 voor alle structurele elementen.

INDEX	DATUM	BESCHRIJVING VAN DE WIJZIGINGEN	ONT.	ENG.
1.1	26/06/2025	Opmerkingen BBT - Gecoördineerd plan	CNN	BOL
1.0	18/06/2025	Opmerkingen BBT+MCW	CNN	BOL
0.2	28/04/2025	Opmerkingen BBT+MCW	CNN	BOL
0.1	28/03/2025	Eerste verzending - ter coördinatie	MPH	BOL

PROJECT :

T&T Lake Side

Site de Tour & Taxis, Av. du Port 88, 1000 Bruxelles

SITUATIE PLAN :

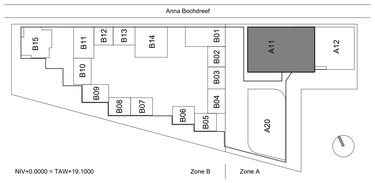

INGENIEUR STABILITEIT :
NEY & PARTNERS s.a. Terhulpensesteenweg, 181 B - 1170 - Brussel tel : +32 2 643 21 90 info@ney.partners

OPDRACHTGEVER :
NEXTENSA Picardstraat 11, B505 B - 1000 - Brussel tel : +32 2 882 10 00 info@nextensa.eu

ARCHITECT :
BUREAU BOUWTECHNIEK Michel de Braeystraat 8 B - 2000 - Antwerpen tel : +32 3 231 53 95 info@b-b.be

INGENIEUR TECHNIEKEN :
CES Straat xxx B - xxxx - yyyy tel : +32 x xxx xx xx info@xxx

HOOFDAANNEMER :
MCW Straat xxx B - xxxx - yyyy tel : +32 x xxx xx xx info@xxx

VERZENDER :

NEY +PARTNERS

PLAN TITEL

Bekistingsplan
ZONE A - GEBOUW A11
P.060_Afdek050

FORMAAT: A0 (841x1188)

FASE: **DO**

EERSTE RELEASEDATUM : **26/03/2025**
DATUM LAATSTE HERZIENING : **26/06/2025**

PROJECT	SUBPROJECT	ORIGINATOR	ROLE	SYSTEM	LEVEL	TYPE	NUMBER	INDEX
LSA -	A11 -	NEY	- ST	- FOR -	050 -	CP	- 3160	- 1.1